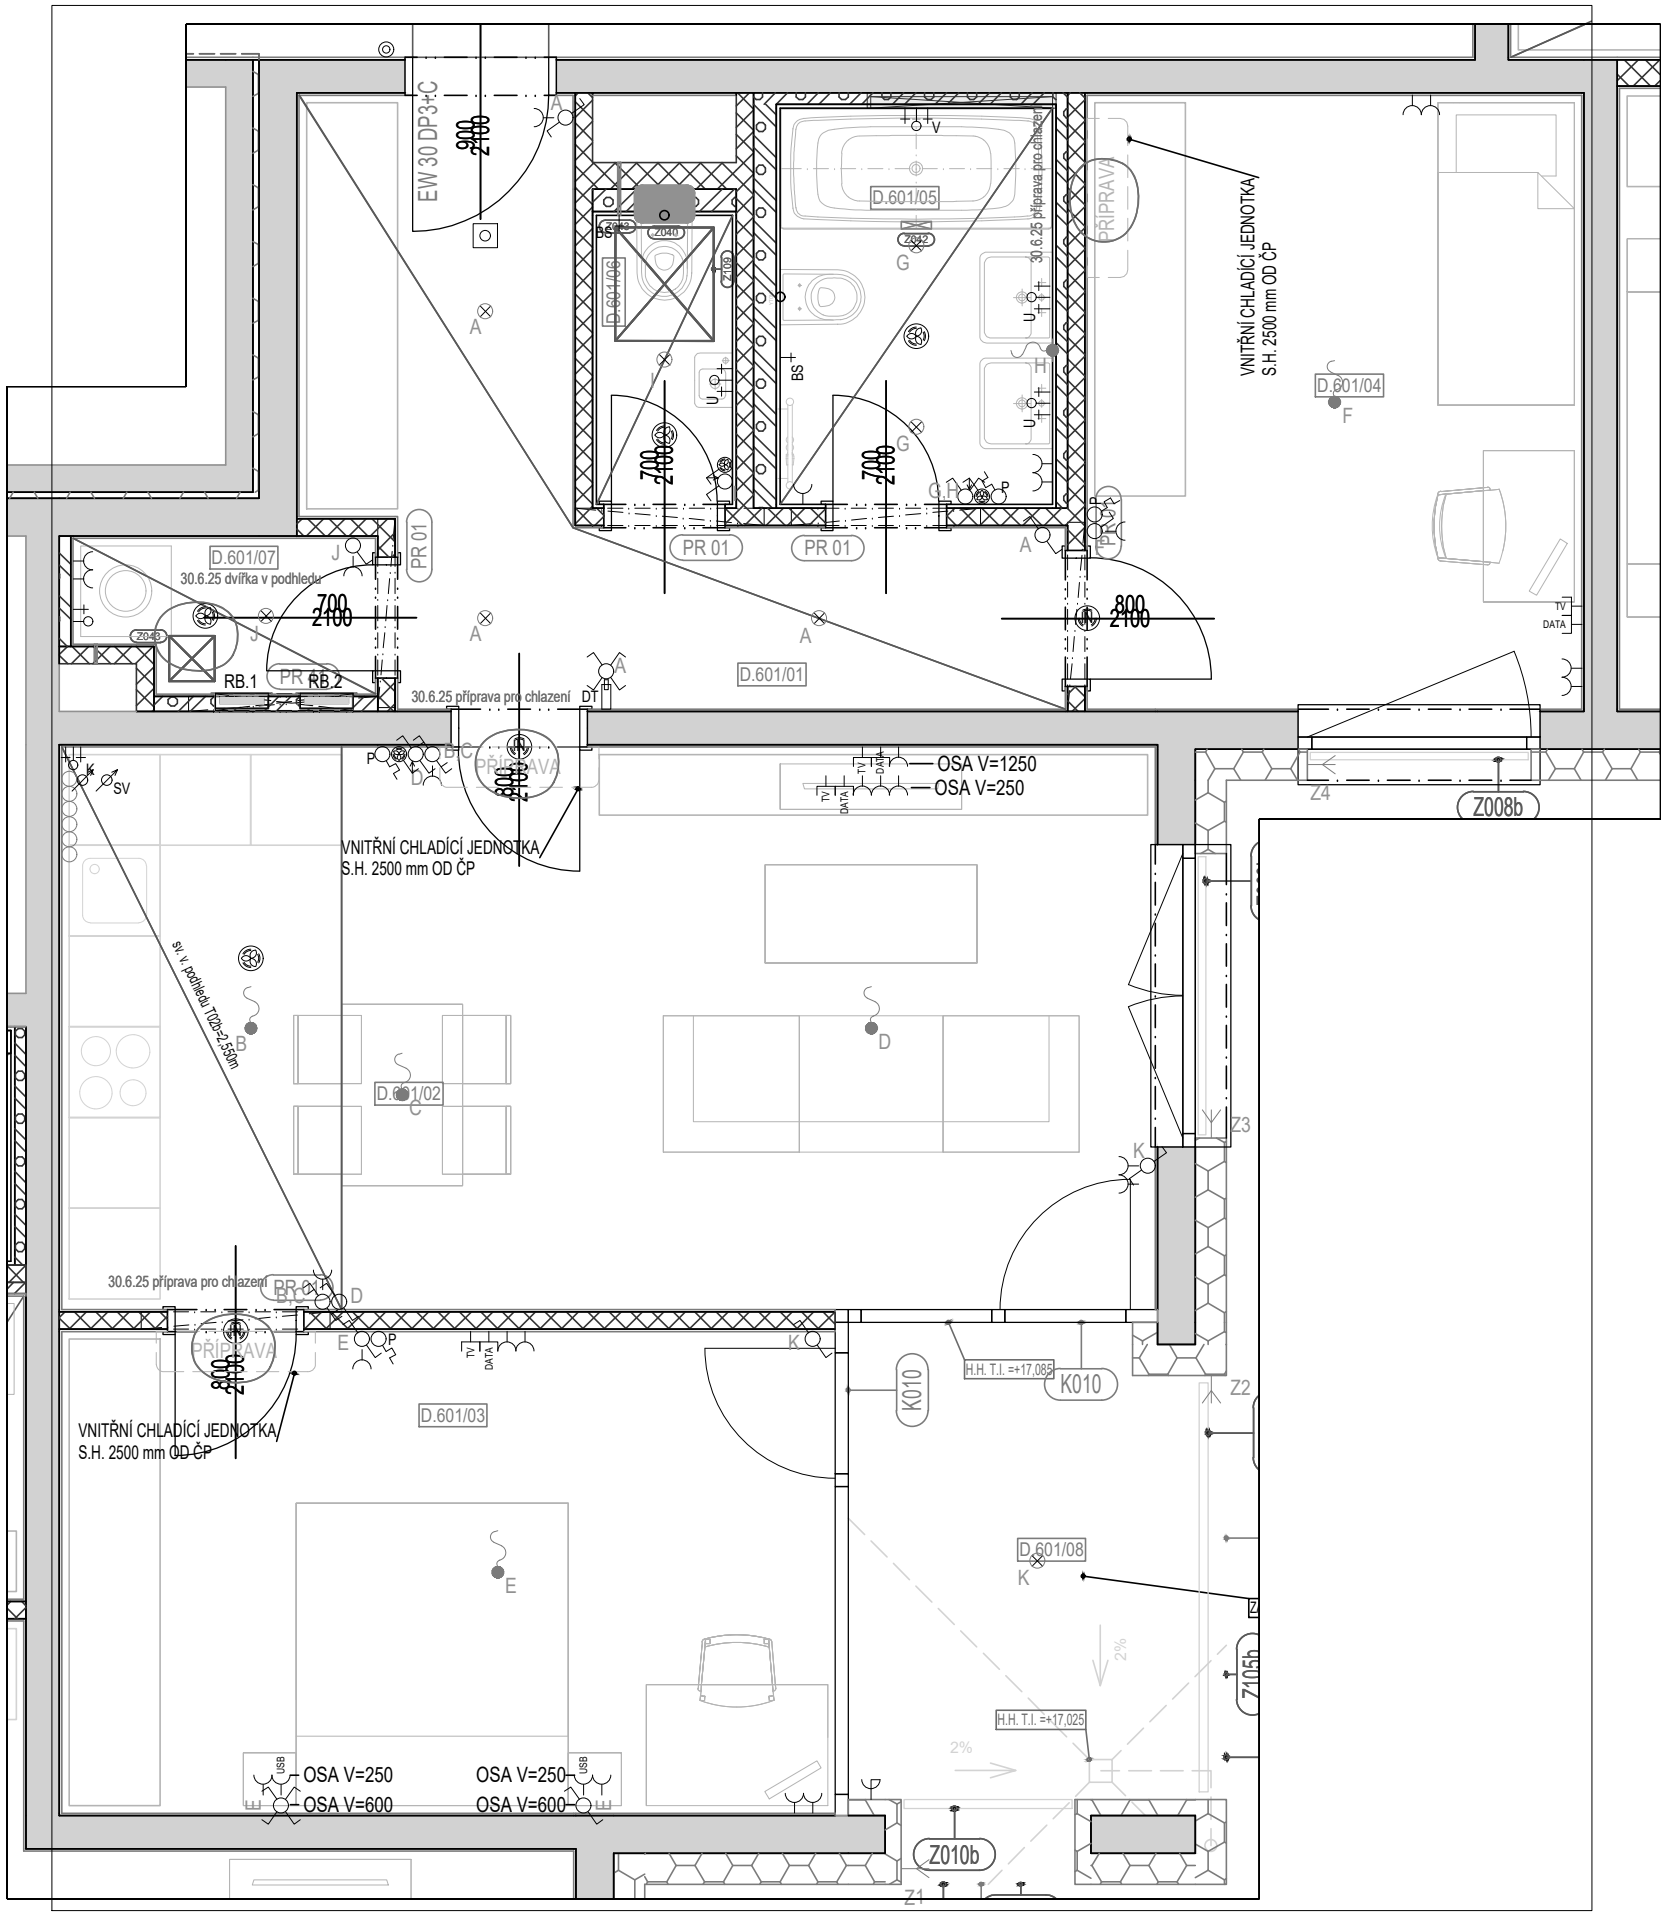

EW 30 DP3+C
2100
900
D.601/05
Z040
Z042
Z039
D.601/06
BS
V
U
G
H
30.6.25 příprava pro chlazení
PŘÍPRAVA
VNITŘNÍ CHLADÍCÍ JEDNOTKA
S.H. 2500 mm OD ČP
D.601/04
F
PR 01
700
2100
D.601/07
30.6.25 dvířka v podhledu
Z043
RB.1
RB.2
D.601/01
800
TV
DATA
DT
OSA V=1250
OSA V=250
Z4
Z008b
SV
sv. v. podhledu T02b=2,50m
B
C
D.601/02
D
Z3
K
Z2
30.6.25 příprava pro chlazení
RB.01
E
P
K010
H.H. T.I. =+17,085
D.601/03
D.601/08
Z105b
2%
H.H. T.I. =+17,025
USB
OSA V=250
OSA V=600
Z010b
Z1